


Proposed Layout Plan: Food Establishment

Kopi & Kaya Toast House Pte. Ltd. (UEN 202355555E)

10 Jalan Besar #01-12, Singapore 208787. Ground floor unit of a shophouse. Total floor area 48 sqm.

CLIENT Kopi & Kaya Toast House Pte. Ltd.	PREMISES 10 Jalan Besar #01-12, S 208787	USE Cafe: kaya toast, eggs, kopi and teh	SEATING 24 seats (6 tables of 4)
--	--	--	-------------------------------------

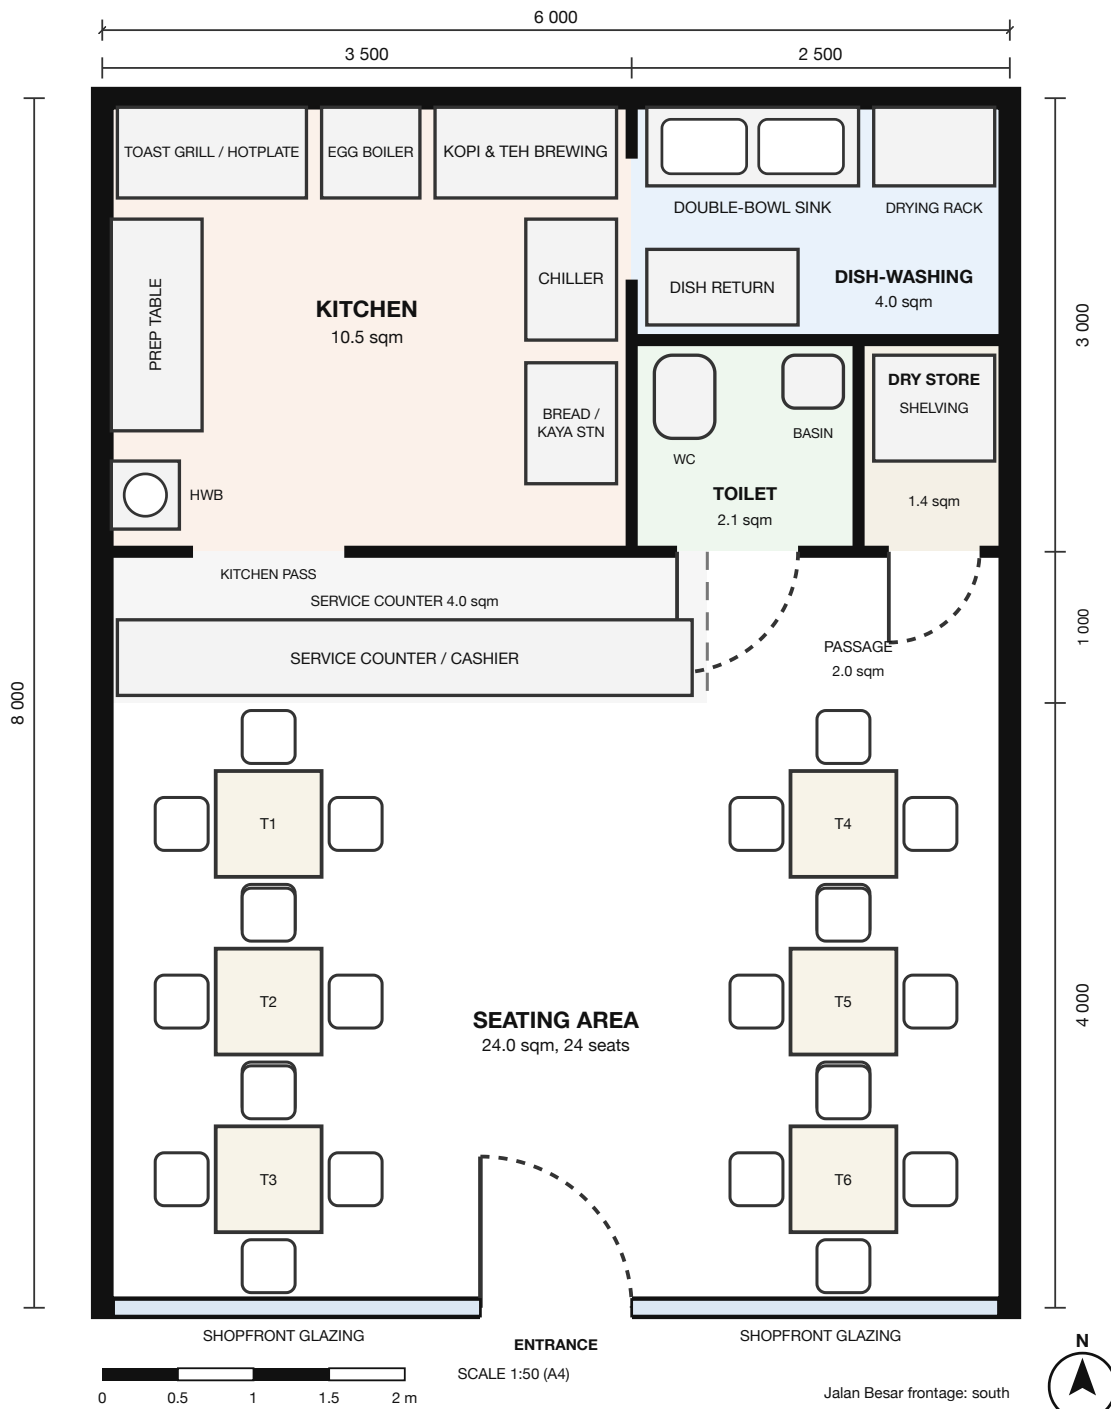



1. Area schedule

Ref	Zone	Dimensions (m)	Area (sqm)	Remarks
K	Kitchen	3.50 x 3.00	10.5	Toast grill and hotplate, egg boiler, kopi and teh brewing, prep table, chiller, hand-wash basin
D	Dish-washing	2.50 x 1.60	4.0	Double-bowl sink, drying rack, dish return shelf; separated from food preparation
T	Toilet	1.50 x 1.40	2.1	Staff and customer use; WC and basin; door opens to passage, not to kitchen
S	Dry store	1.00 x 1.40	1.4	Shelving for packaged goods, 150 mm off floor
C	Service counter	4.00 x 1.00	4.0	Cashier, order pick-up, display of packaged kaya
P	Passage	2.00 x 1.00	2.0	Access to toilet and store
A	Seating area	6.00 x 4.00	24.0	6 tables of 4 seats (T1 to T6), entrance and shopfront glazing
Total floor area			48.0	Internal, wall to wall

2. Legend

Symbol	Meaning
	External wall (brick, existing)
	Internal partition (new, moisture-resistant board on steel studs)
	Shopfront glazing
	Door with swing
	Fixed equipment or furniture (labelled on plan)
	Table with 4 seats
HWB	Hand-wash basin (hands-free tap, soap and paper towel dispenser)

3. Seating schedule

Table	Type	Seats	Location
T1, T2, T3	Square table 700 x 700 mm, 4 chairs	12	West side of seating area
T4, T5, T6	Square table 700 x 700 mm, 4 chairs	12	East side of seating area
Total seating capacity		24	No standing area proposed

4. Notes

Business	Kopi & Kaya Toast House Pte. Ltd., UEN 202355555E
Menu	Kaya toast, soft-boiled eggs, kopi and teh. No deep frying proposed.
Operating hours	Monday to Sunday, 7:00 am to 9:00 pm
Staff	4 food handlers on the roster; maximum 3 on shift at any time
Ventilation	Kitchen exhaust hood over toast grill and hotplate, ducted to rear; grease filter cleaned weekly
Waste	Covered bins in kitchen and dish-washing; grease trap under dish-washing sink; refuse to rear bin point
Finishes	Kitchen and dish-washing: non-slip tiles, tiled walls to 1.8 m, coved skirting; seating: vinyl plank
Pest proofing	Fly screens to rear opening; door sweeps to entrance and rear door

R. Lim
Rachel Lim
Prepared by, Lim & Ong Design Studio (fictional)
20 October 2025

Tan Wei Ling
Tan Wei Ling
Accepted for Kopi & Kaya Toast House Pte. Ltd., Director
22 October 2025

Fictional document produced for a software demonstration. Not issued by any authority. The design practice, the persons and the drawing references in this document are invented. The plan is illustrative and is not a survey of any real premises.